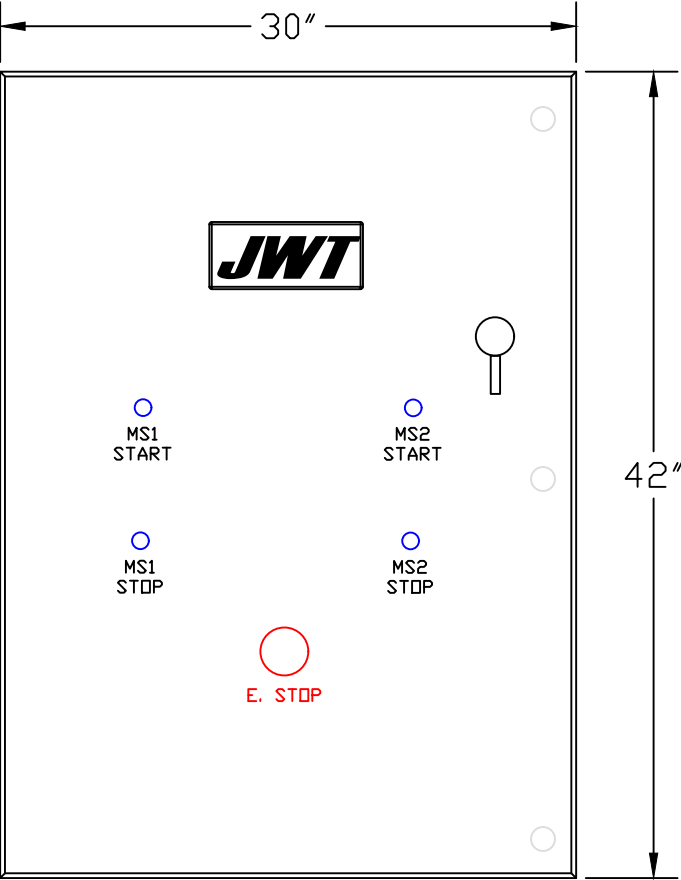
 



NEMA 4 PAINTED STEEL

PUMP HP: 5.2 AT DUTY POINT
PUMP DRAWS 8 AMPS AT 460V. MCA:10 I MOP:18

CUSTOMER: - - DRAWING NUMBER: -						JOE WHITE TANK	
PURCHASE ORDER NUMBER: -						2710 N NICHOLS ST, FORT WORTH, TX 76106 (817) 624-1141	
TITLE: STARTER PANEL TWO 5A PUMPS WIRING DIAGRAM				PD DATE: -		TOLERANCES	
						UNLESS OTHERWISE SPECIFIED	
						DECIMAL: X.XXX ±0.005" FRACTIONAL: ±1/8" ANGULAR: ±1°	
DRAFT BY		ENG.	PROJ. MNGR	REVISION	SHEET NUMBER	PROPRIETARY INFORMATION	
RD		FW	SY	A	1 OF 4	THIS DRAWING IS THE PROPERTY OF JOE WHITE TANK CO. ANY REPRODUCTION OR USE OF THIS DRAWING MUST BE APPROVED	
SCALE		N.T.S.					

A	FDR APPROVAL	01/15/2026	RD
NO	REVISION	DATE	BY


FROM UL LISTED CIRCUIT BREAKER OR FUSED
DISCONNECT
PROTECTED POWER SOURCE. 460VAC/60HZ/3PH, 65KAIC

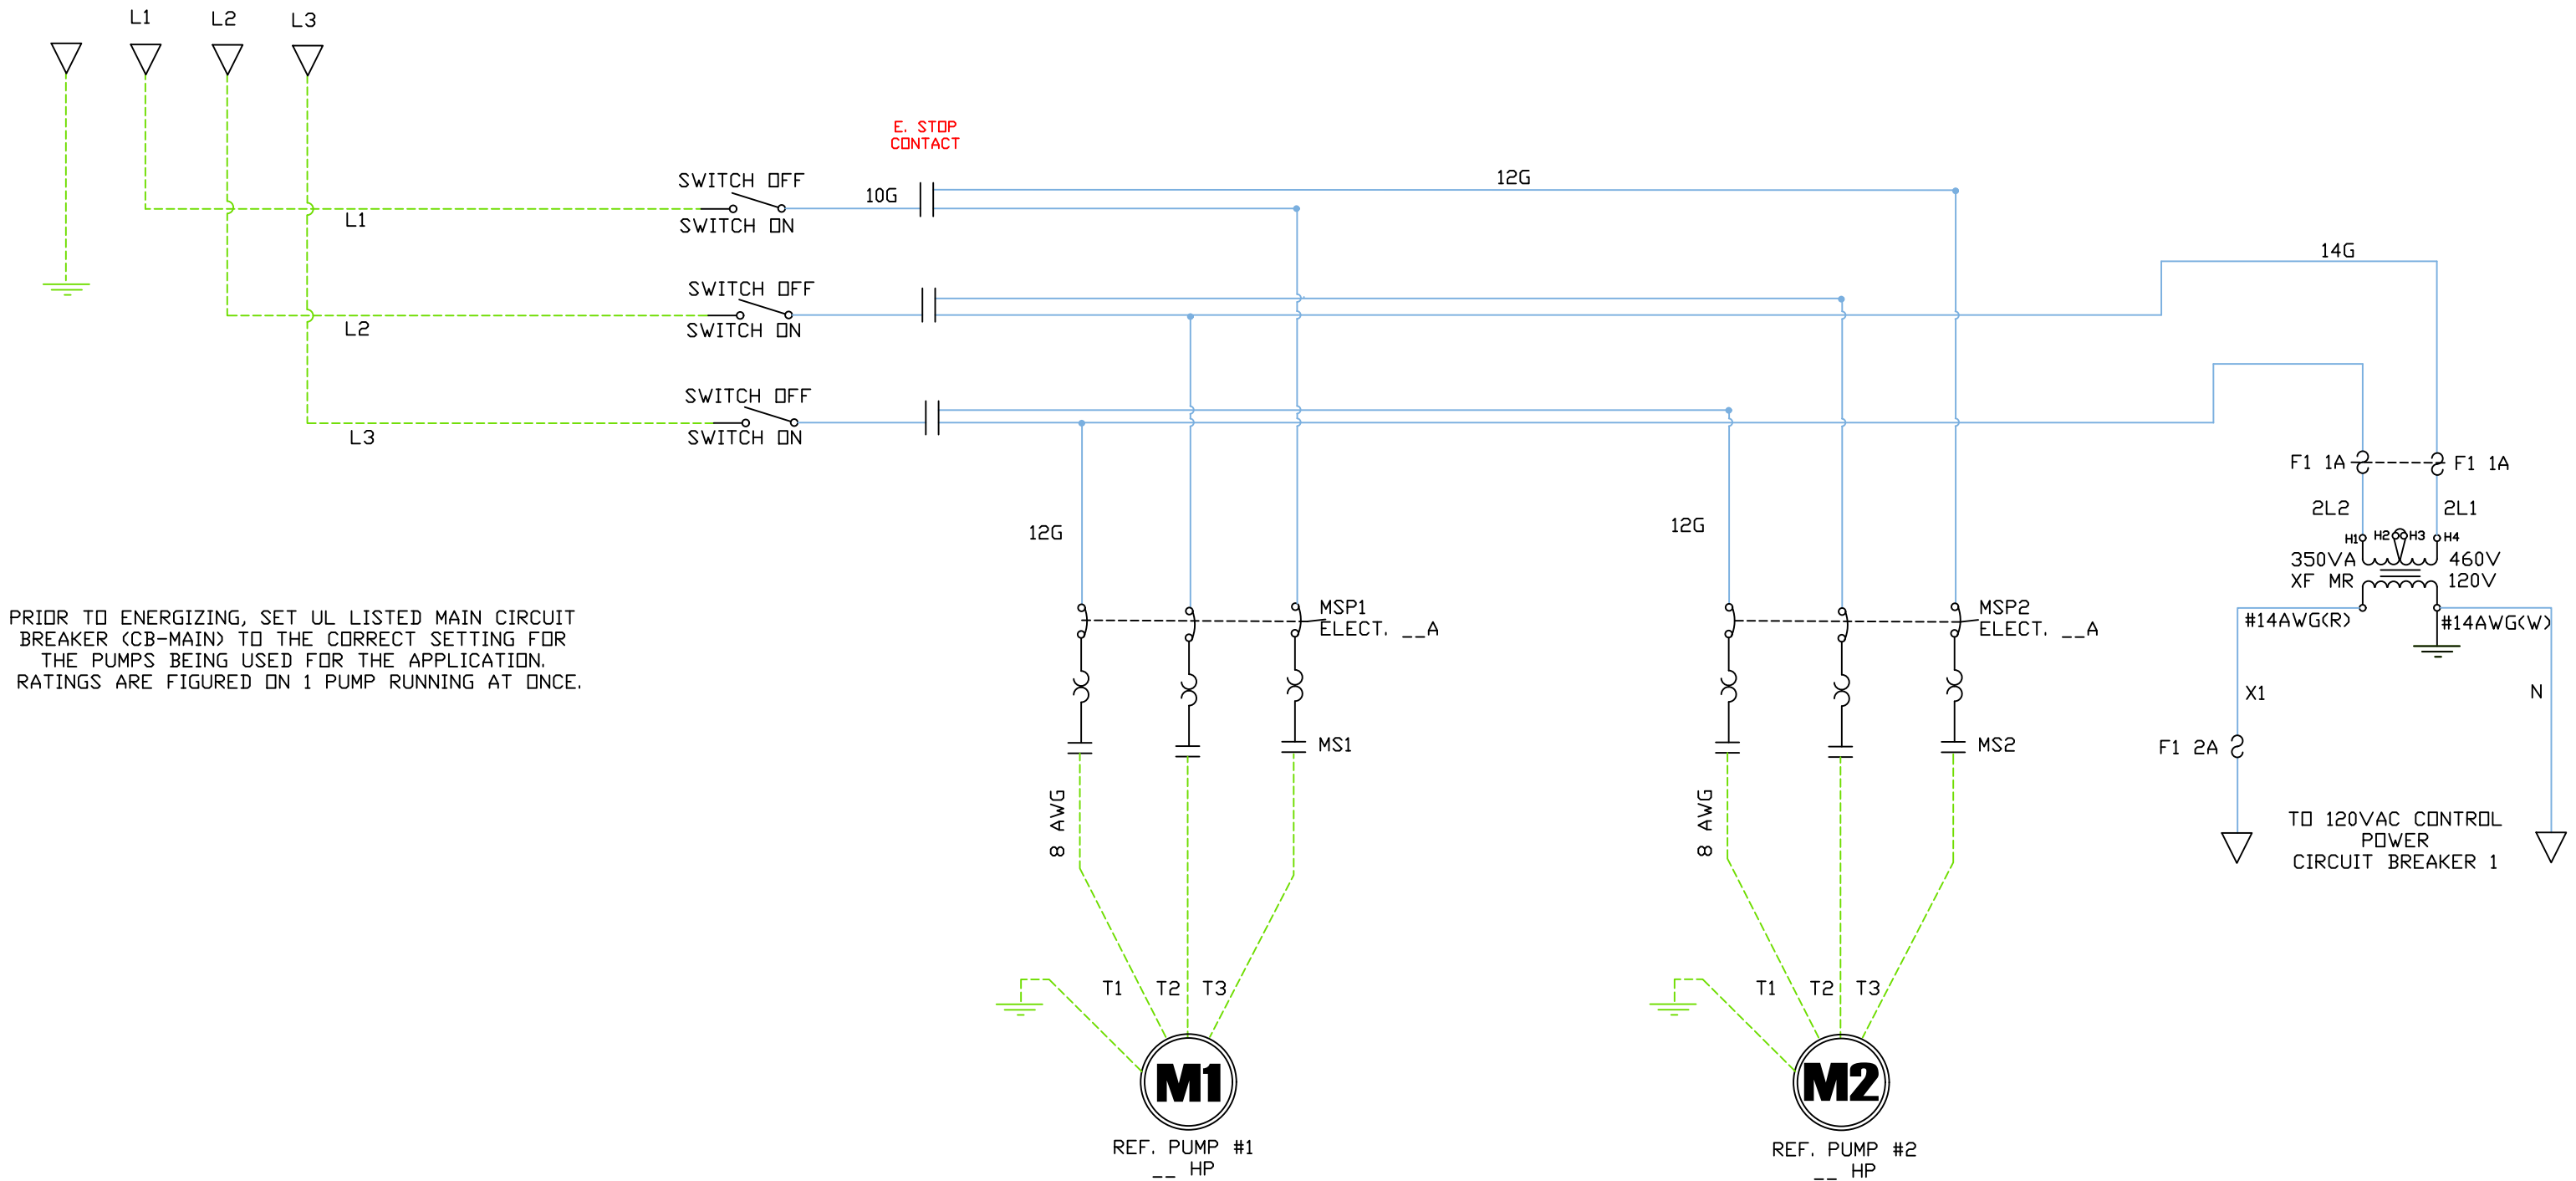


ALL FIELD CONTROL WIRING TO BE #14AWG MINIMUM UNLESS OTHERWISE SPECIFIED BY LOCAL CODES.
CONSULT MANUFACTURER'S WIRING RECOMMENDATION FOR TYPE, SIZE, AND TERMINATION REQUIREMENT AS RELATED TO THE APPLICATION.

(R) RED WIRE - 120VAC HOT
(W) WHITE WIRE - 120VAC NEUTRAL
(G) GREEN GROUND WIRE

CUSTOMER:		JOE WHITE TANK	
-		2710 N NICHOLS ST, FORT WORTH, TX 76106	
DRAWING NUMBER: -		(817) 624-1141	
PURCHASE ORDER NUMBER: -		PD DATE: -	
TITLE: STARTER PANEL TWO 5A PUMPS WIRING DIAGRAM		TOLERANCES	
DRAFT BY: RD		UNLESS OTHERWISE SPECIFIED	
ENG: EW		DECIMAL: XXXX ±0.005"	
PROJ. MNGR: SY		FRACTIONAL: ±1/8"	
REVISION: A		ANGULAR: ±1°	
SHEET NUMBER: 1 OF 4		SCALE: N.T.S.	
NO		PROPRIETARY INFORMATION	
REVISION		THIS DRAWING IS THE PROPERTY OF JOE WHITE TANK CO.	
DATE		ANY REPRODUCTION OR USE OF THIS DRAWING MUST BE APPROVED	
BY			

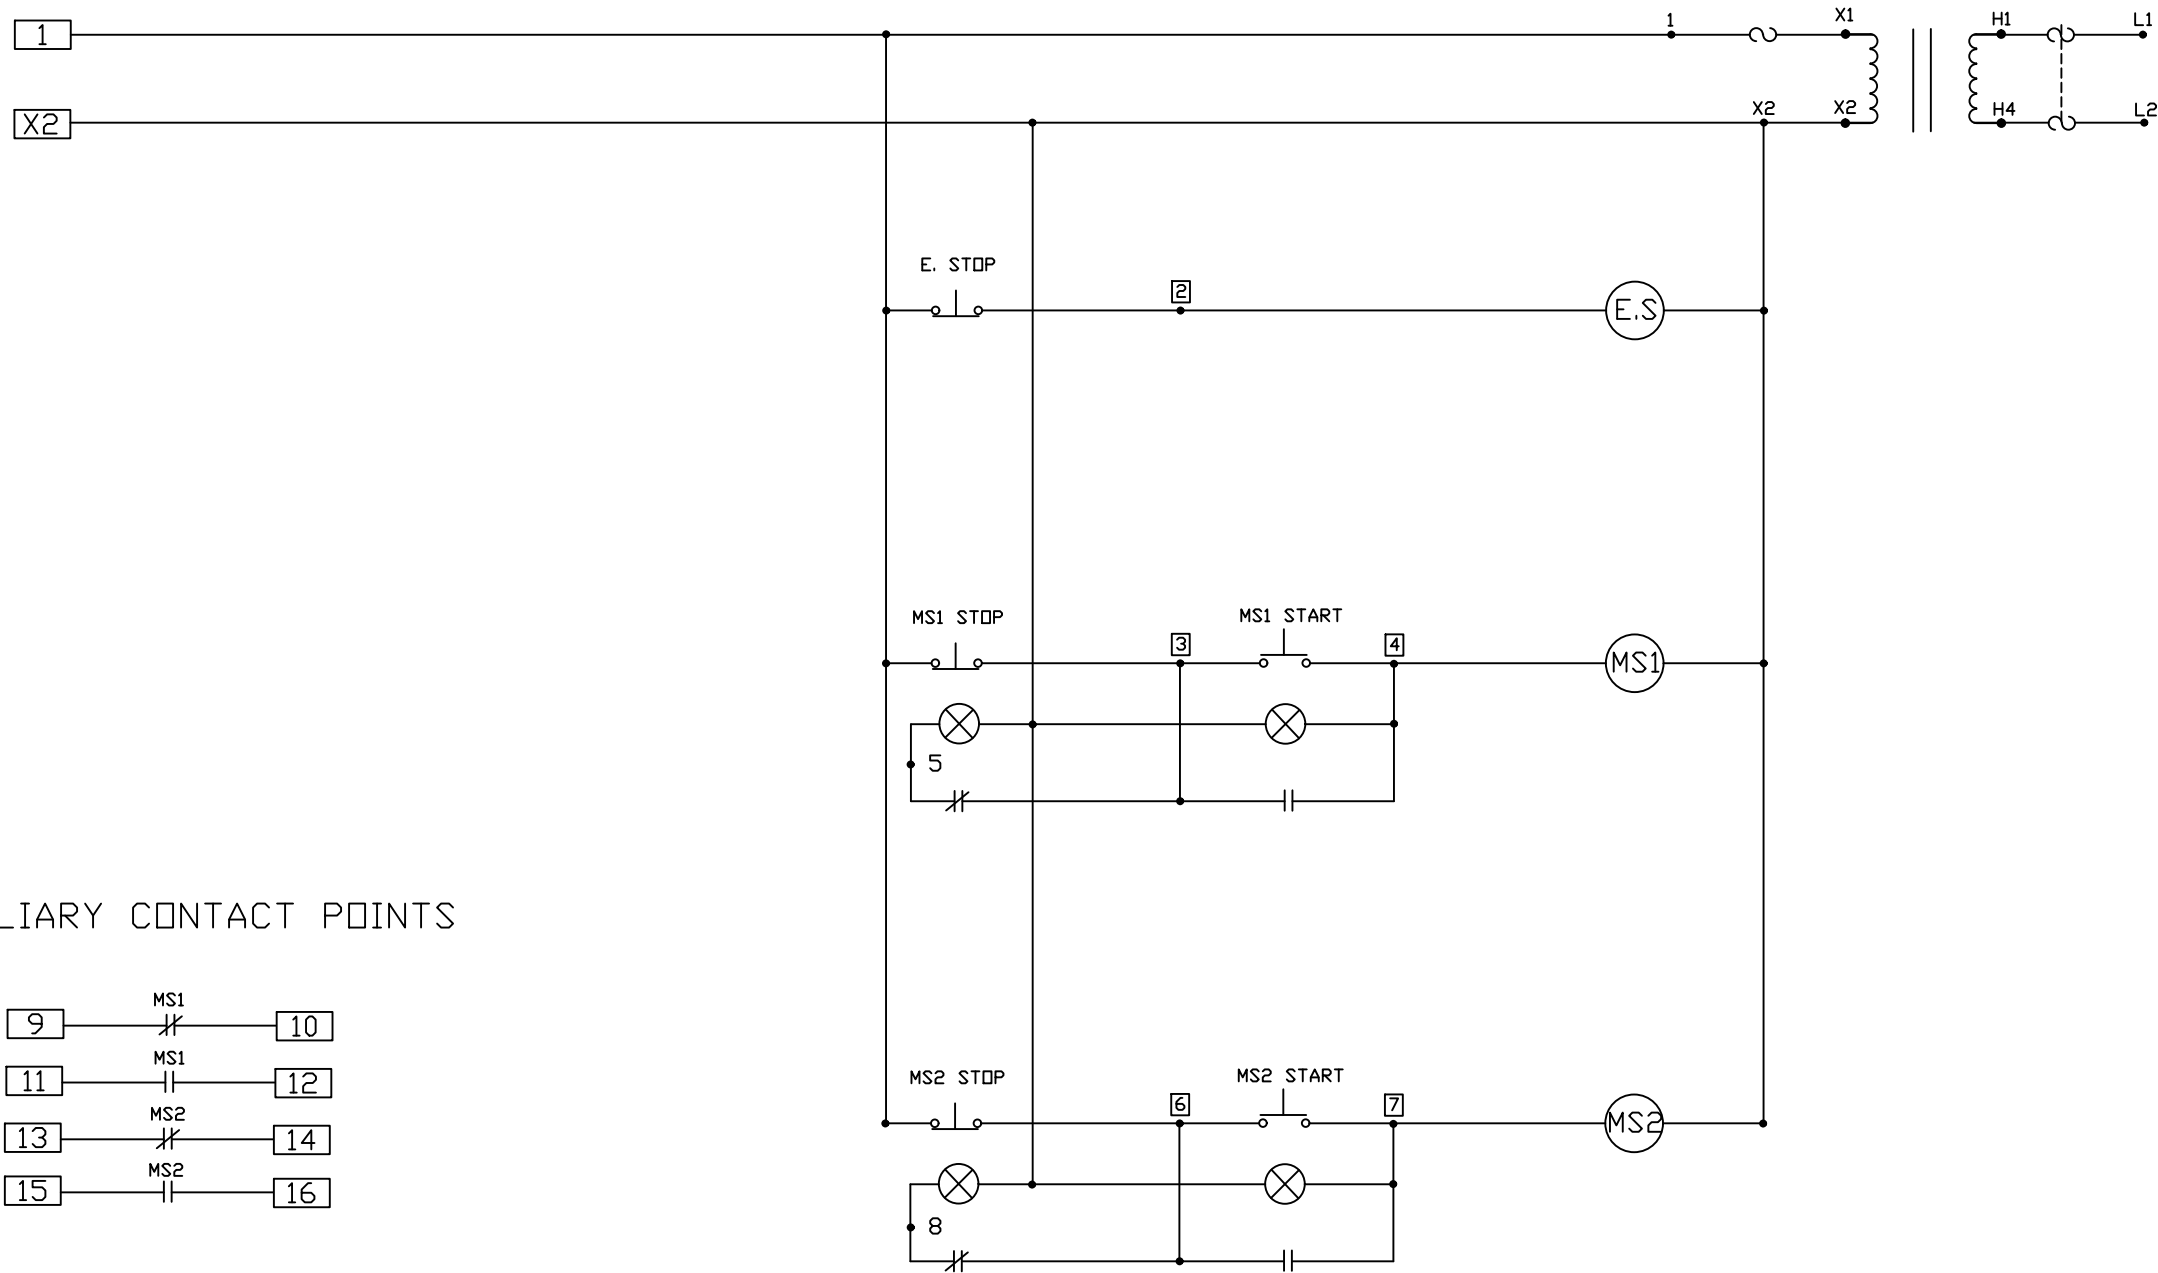

AUXILIARY CONTACT POINTS

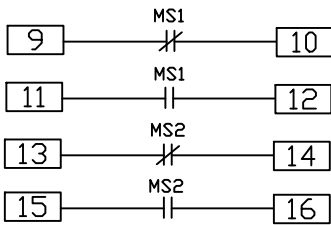

SCHEMATIC DIAGRAM

(R) RED WIRE - 120VAC HOT
(W) WHITE WIRE - 120VAC NEUTRAL
(G) GREEN GROUND WIRE

CUSTOMER:
-

JOE WHITE TANK
2710 N NICHOLS ST, FORT WORTH, TX 76106
(817) 624-1141

DRAWING NUMBER: -

PD DATE: -

PURCHASE ORDER NUMBER: -

TOLERANCES
DECIMAL: X.XXX ±0.005" FRACTIONAL: ±1/8" ANGULAR: ±1°


TITLE: STARTER PANEL TWO 5A PUMPS WIRING DIAGRAM

UNLESS OTHERWISE SPECIFIED


DRAFT BY	ENG.	PROJ. MNGR	REVISION	SHEET NUMBER	SCALE
RD	EW	SY	A	1 OF 4	N.T.S.

PROPRIETARY INFORMATION
THIS DRAWING IS THE PROPERTY OF JOE WHITE TANK CO.
ANY REPRODUCTION OR USE OF THIS DRAWING MUST BE APPROVED

A	FDR APPROVAL	01/15/2026	RD
NO	REVISION	DATE	BY

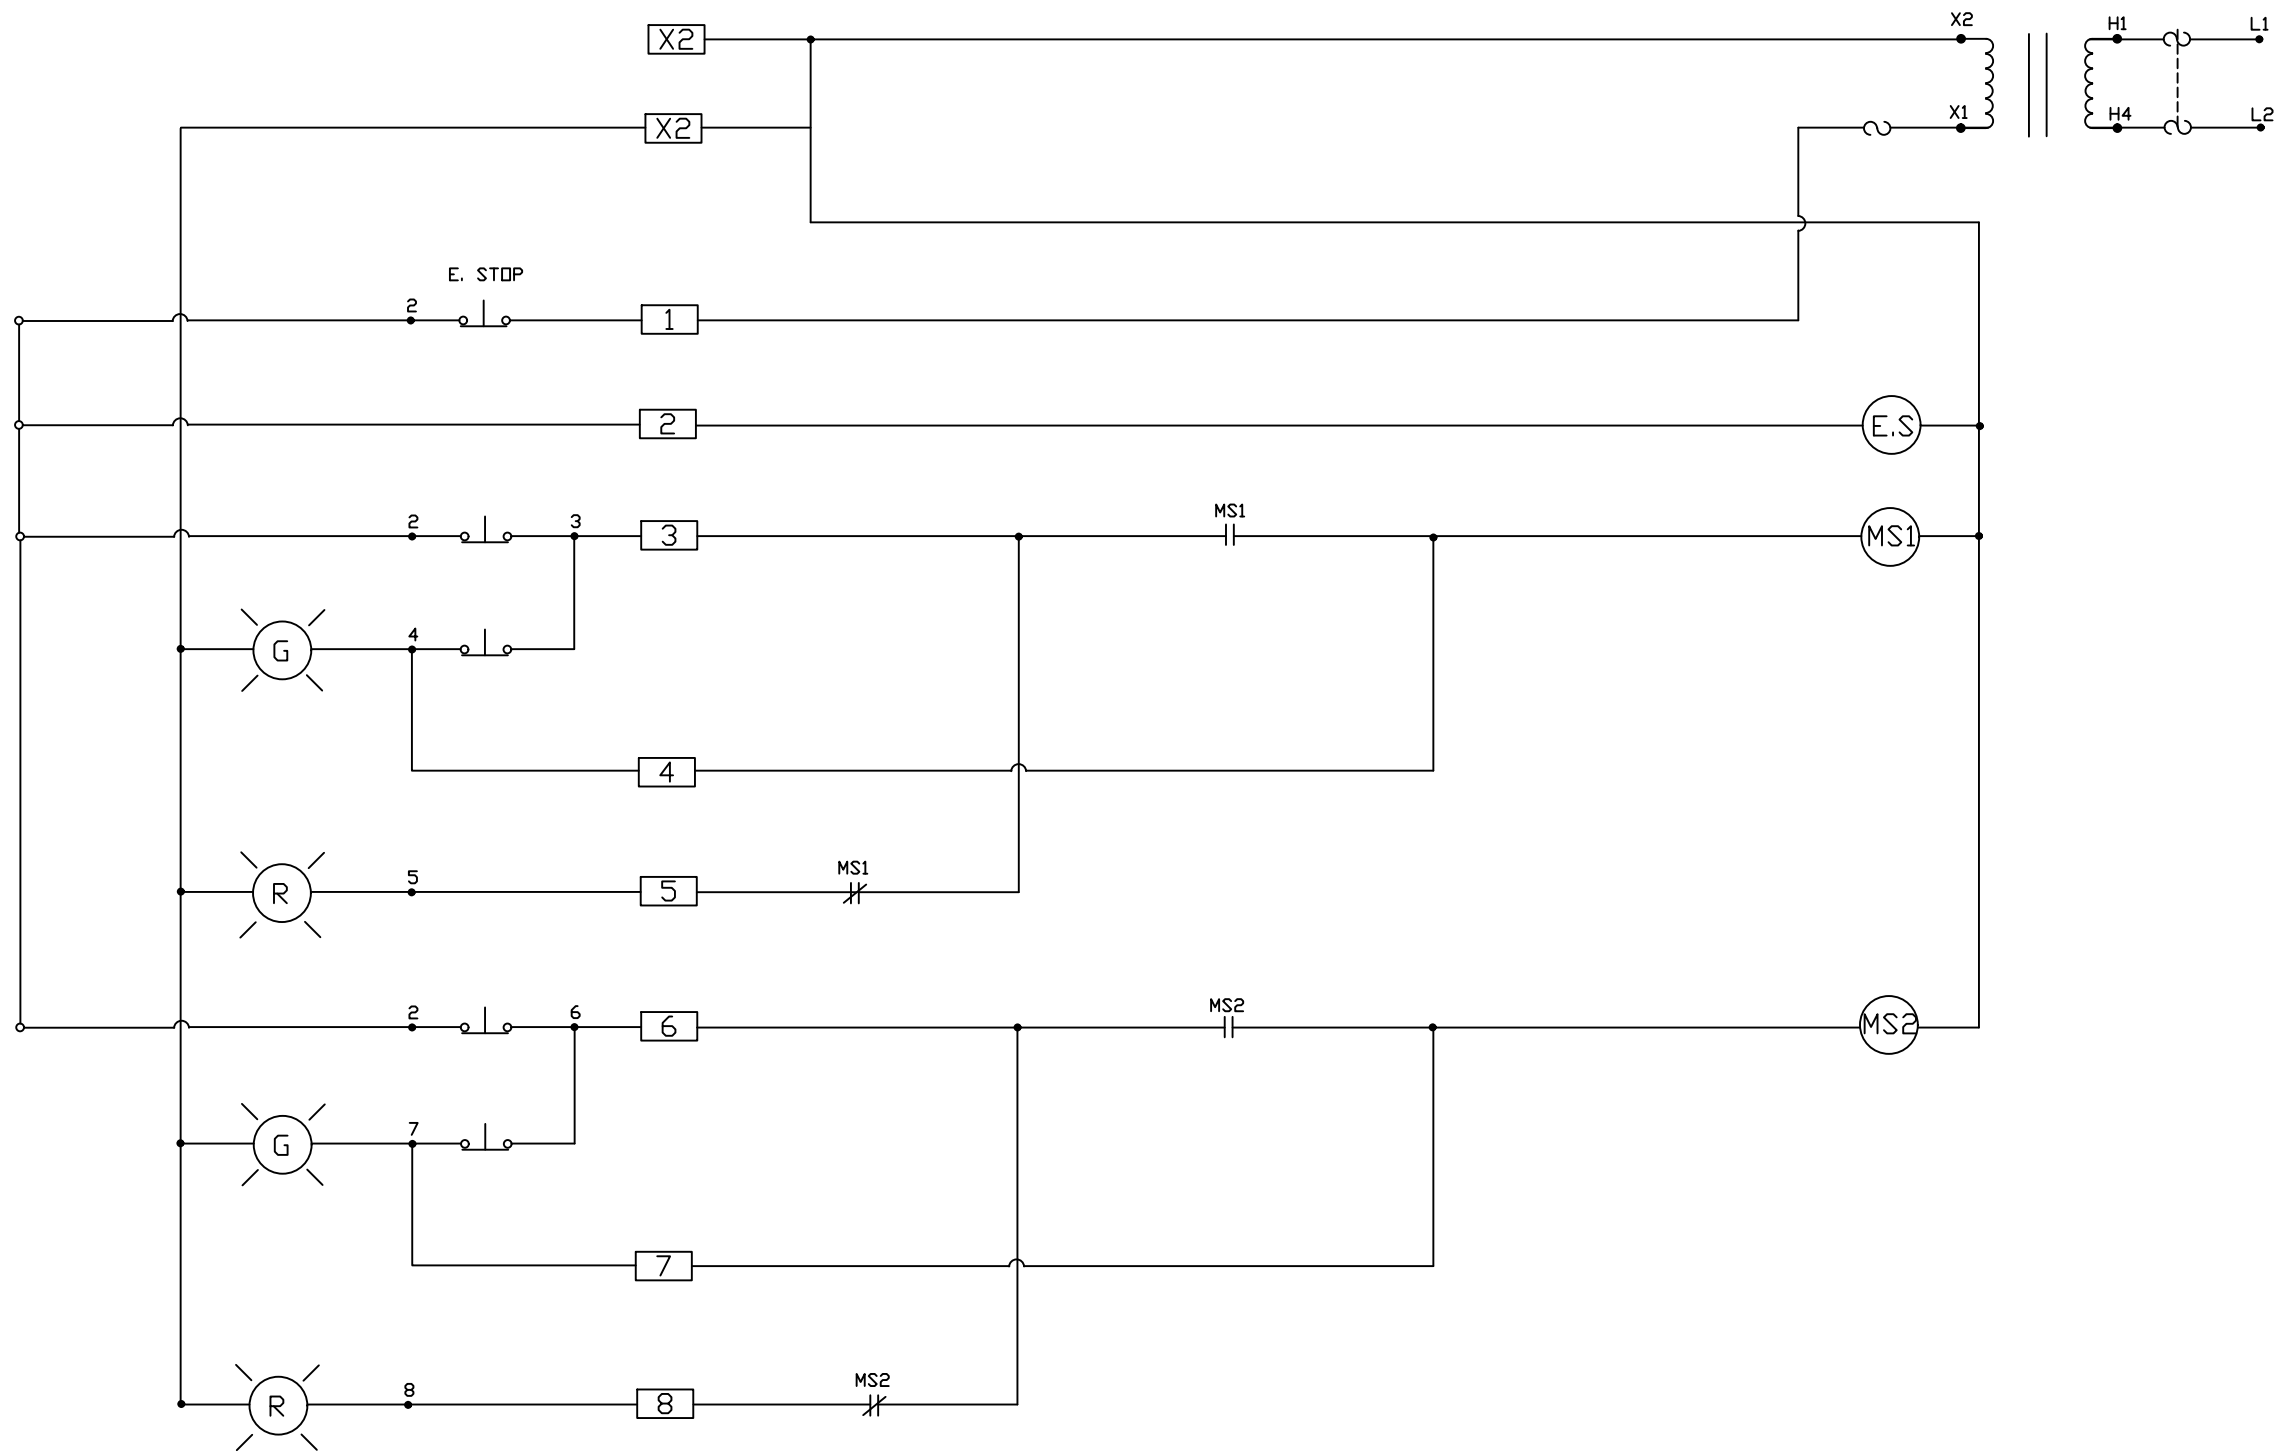

AUXILIARY CONTACT POINTS

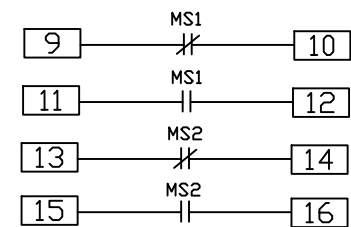

WIRING DIAGRAM

CUSTOMER:		-	
DRAWING NUMBER:		-	
PURCHASE ORDER NUMBER:		-	
TITLE: STARTER PANEL TWO 5A PUMPS WIRING DIAGRAM		PD DATE: -	
TOLERANCES		UNLESS OTHERWISE SPECIFIED	
DECIMAL: X.XXX ±0.005"		FRACTIONAL: ±1/8"	
ANGULAR: ±1°		ANGULAR: ±1°	
PROPRIETARY INFORMATION		THIS DRAWING IS THE PROPERTY OF JOE WHITE TANK CO.	
ANY REPRODUCTION OR USE OF THIS DRAWING MUST BE APPROVED		ANY REPRODUCTION OR USE OF THIS DRAWING MUST BE APPROVED	

A	FOR APPROVAL	01/15/2026	RD
NO	REVISION	DATE	BY

DRAFT BY	ENG.	PROJ. MNGR	REVISION	SHEET NUMBER	SCALE
RD	FW	SY	A	1 OF 4	N.T.S.